

PROPOSED TOWNSHIP GERARDSVILLE EXTENSION 4

SITUATED ON
PORTIONS 16 & 66 OF THE FARM KNOPIESLAAGTE 385-JR

GENERAL INFORMATION:

ZONING:	LAND USE:	ERF NUMBER:	TOTAL ERVEN:	AREA:	% OF TOWN:
	AGRICULTURAL	1 TO 15	15	131,1828Ha	93,00%
	INFRASTRUCTURE WORKS	16	1	3,1586Ha	2,24%
	STREET	17 & 18	2	6,7091Ha	4,76%
	TOTAL		18	141,0505Ha	100,0%

NOTES:


1. ALL DIMENSION ARE APPROXIMATE AND SUBJECT TO FINAL SURVEY.
2. PROPOSED 25,0m ACCESS ROAD, SUBJECT TO GEOTECHNICAL & DOLOMITE INVESTIGATION.
3. 22,0m ELECTRICAL POWER TRANSMISSION SERVITUDE VIDE SG DIAGRAM 2337/2000.
4. 15,74m R.O.W. SERV VIDE SG DIAGRAM A5592/1952.
5. 15,0m R.O.W. AND PIPELINE SERV VIDE SG DIAGRAM 1595/2022.

2 AUGUST 2024

LEGEND:

- TOWNSHIP BOUNDARY
- 32,0m BUFFER
- GEOLOGICAL ZONES
- ENVIRONMENTAL SENSITIVITIES
- 1:50 YEAR FLOOD LINE
- 1:100 YEAR FLOOD LINE
- LINE OF NO ACCESS
- PROPOSED RIGHT OF WAY SERVITUDE

LOCALITY MAP:

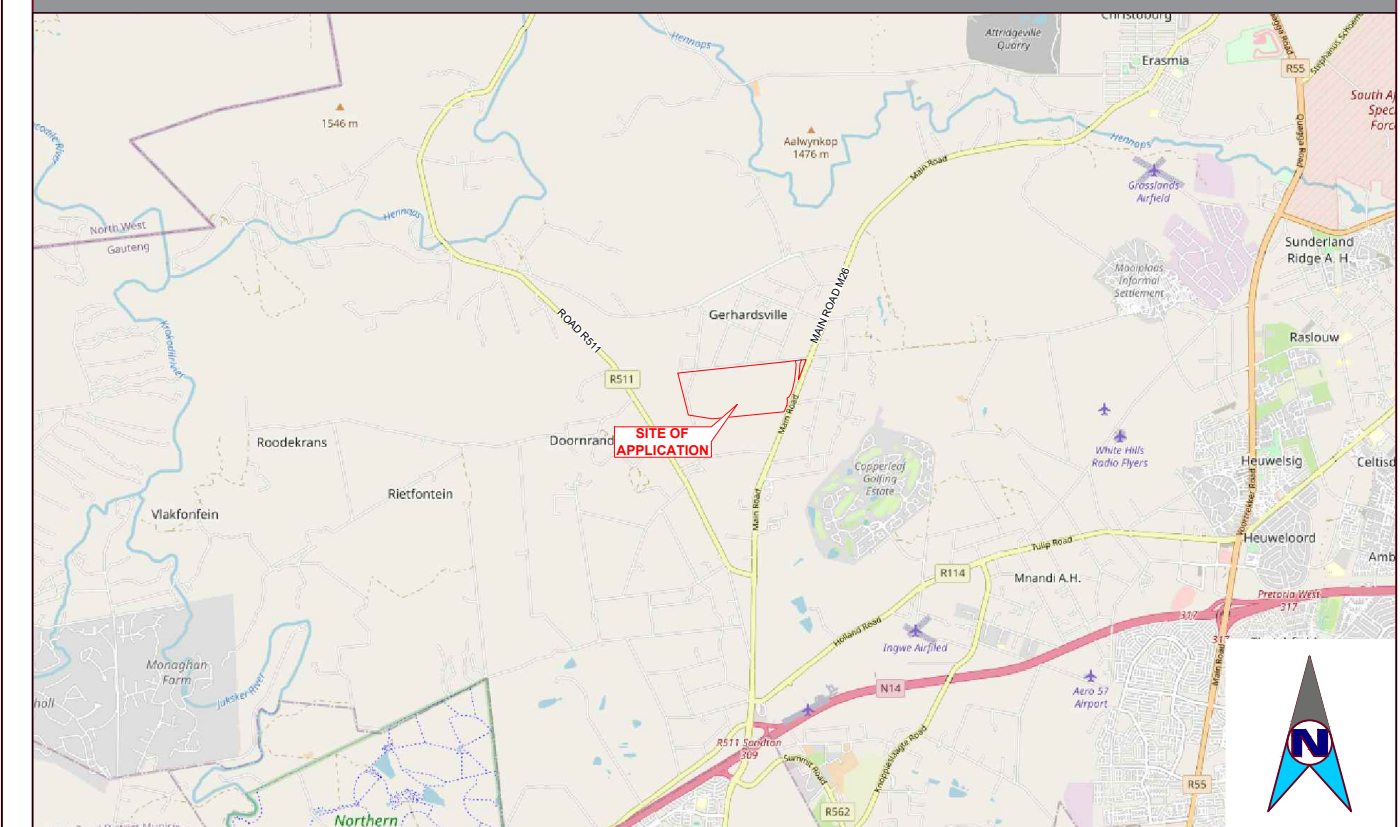

P. O. Box 35921
Menlo Park
South Africa
0102


61 Thomas Edison Street
Menlo Park
South Africa
0081

Tel: +27 (12) 346 7890
Fax: +27 (86) 538 1064

E-mail: draw@dlcgroup.co.za
www.dlcgroup.co.za

COPYRIGHT

Company Reg nr: 2002/025882/07

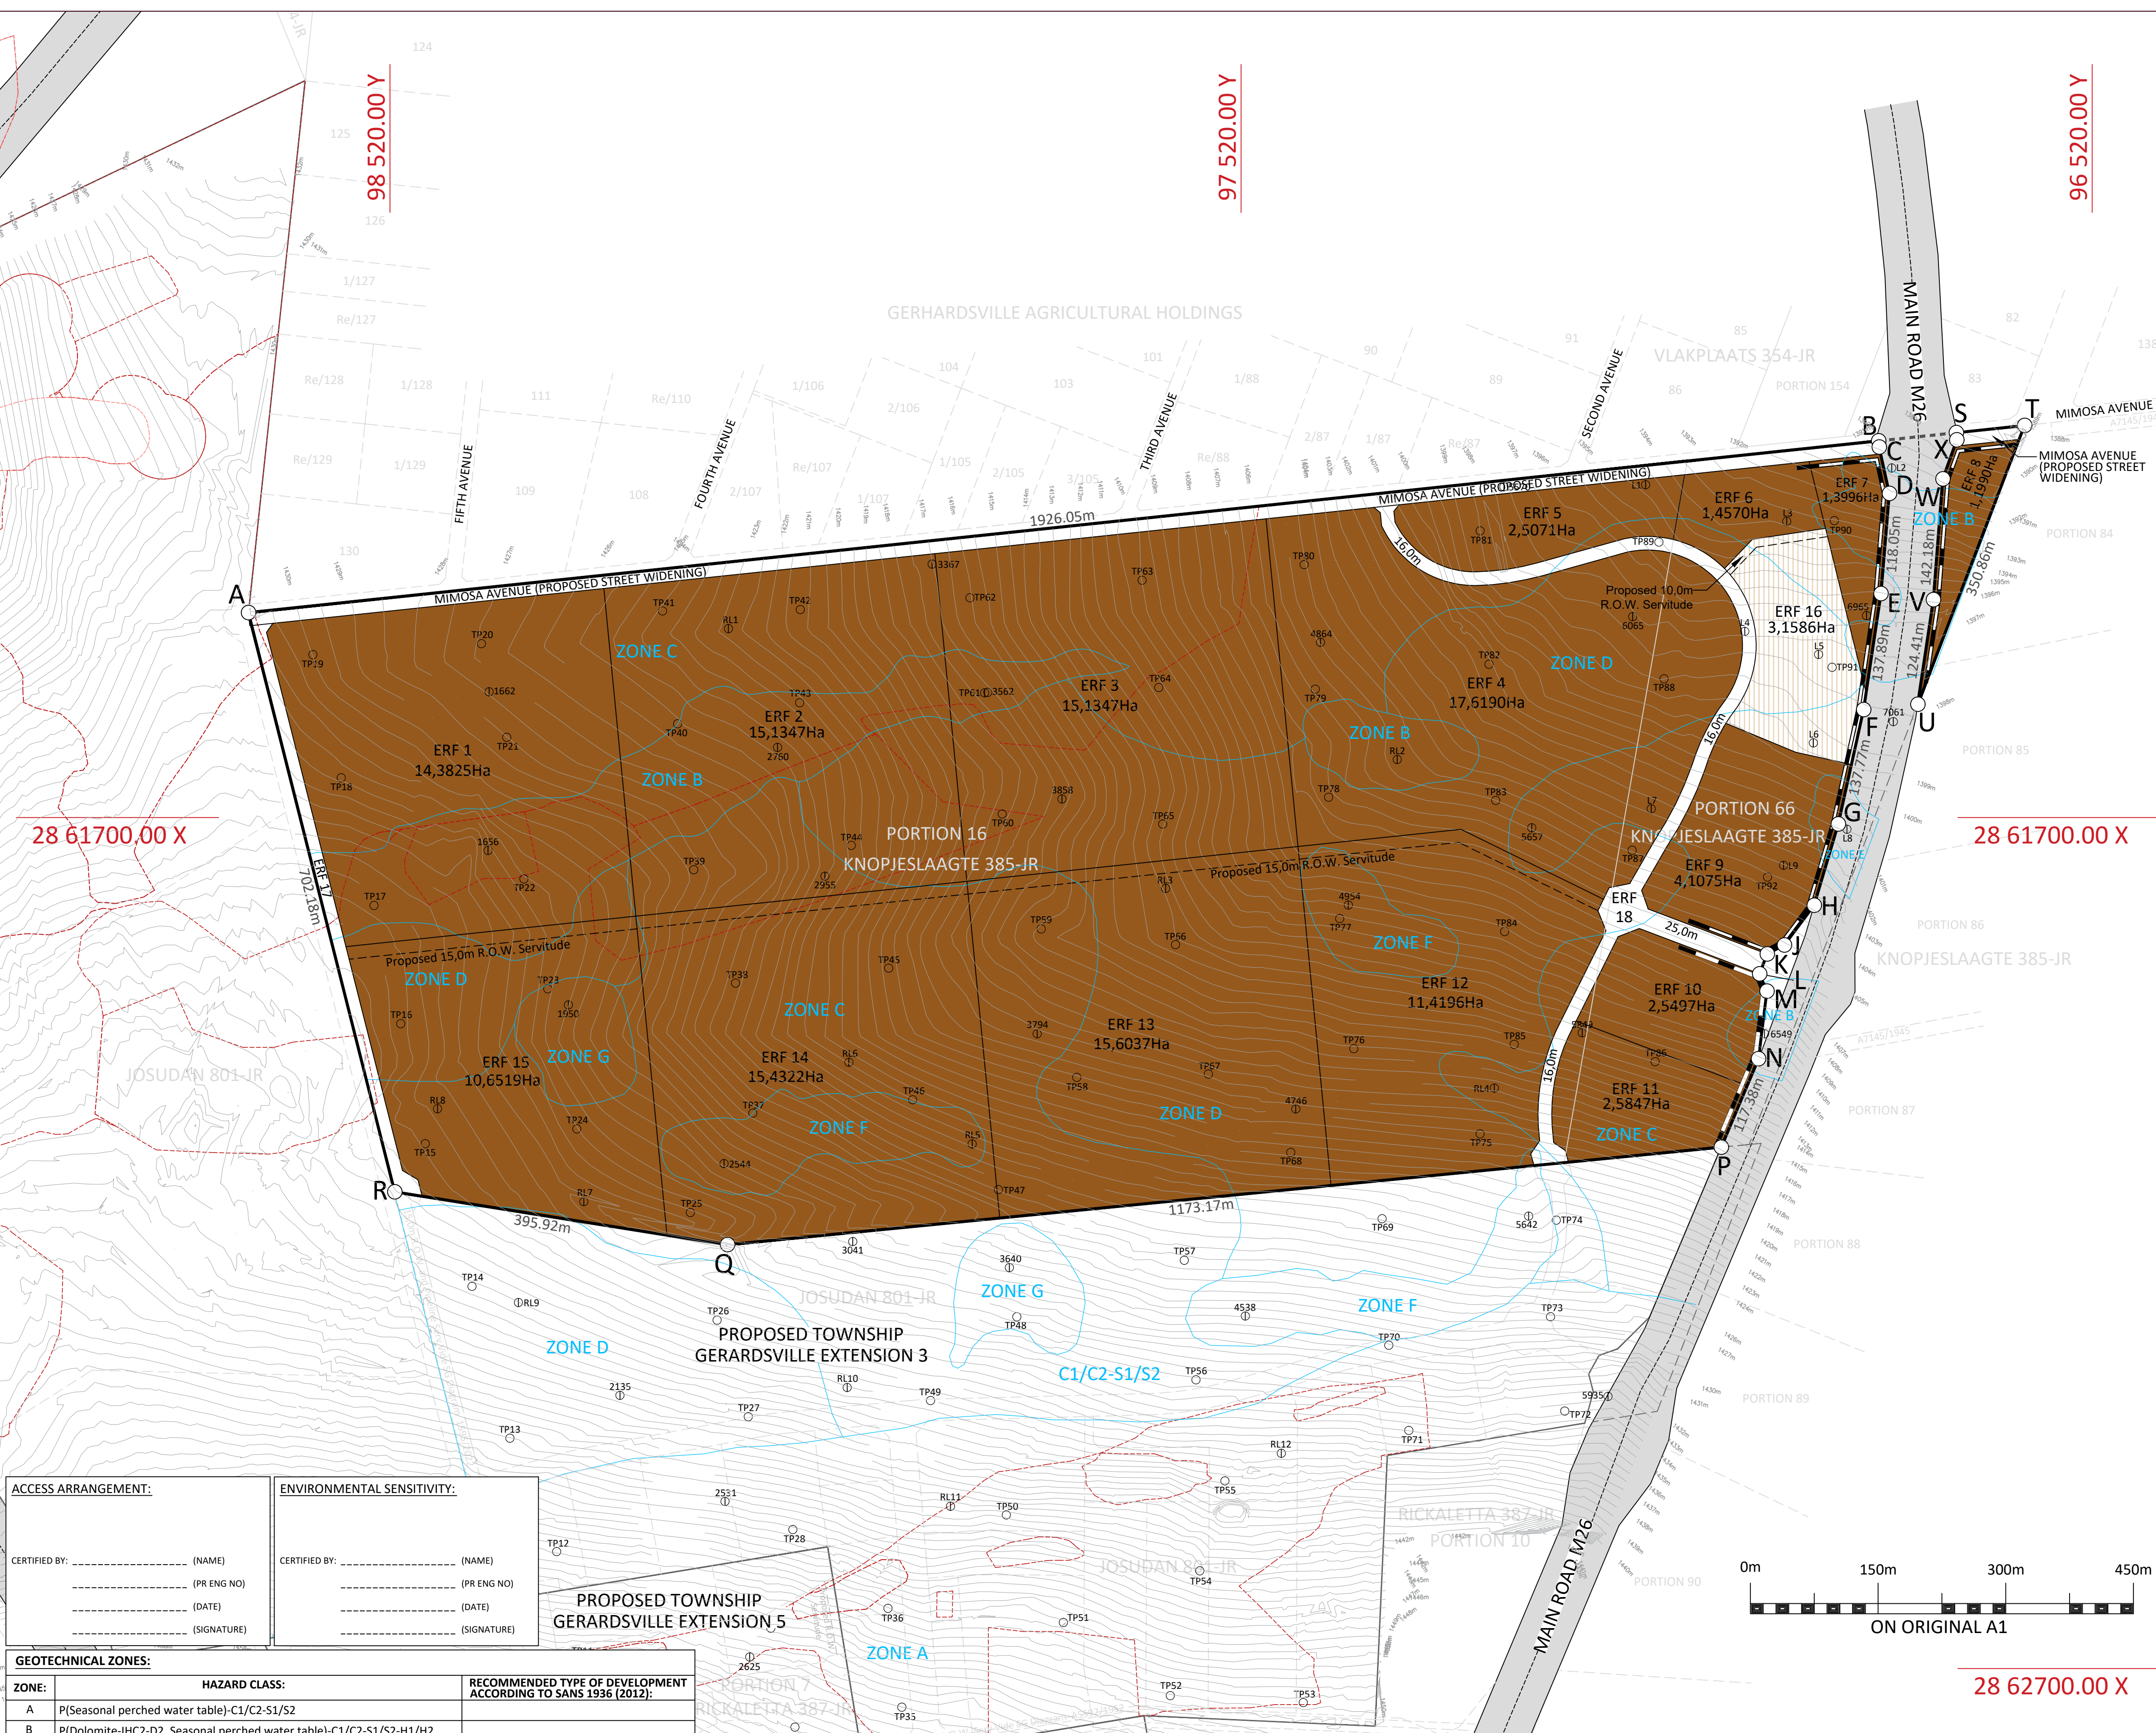

ACCESS ARRANGEMENT:	ENVIRONMENTAL SENSITIVITY:
CERTIFIED BY: _____ (NAME)	CERTIFIED BY: _____ (NAME)
_____ (PR ENG NO)	_____ (PR ENG NO)
_____ (DATE)	_____ (DATE)
_____ (SIGNATURE)	_____ (SIGNATURE)

GEOTECHNICAL ZONES:		
ZONE:	HAZARD CLASS:	RECOMMENDED TYPE OF DEVELOPMENT ACCORDING TO SANS 1936 (2012):
A	P(Seasonal perched water table)-C1/C2-S1/S2	
B	P(Dolomite-IHC2-D2, Seasonal perched water table)-C1/C2-S1/S2-H1/H2	
C	P(Dolomite-IHC3/4/5-D3, Seasonal perched water table)-C1/C2-S1/S2	
D	P(Dolomite-IHC3/4/5-D3, Seasonal perched water table)-C1/C2-S1/S2-H1/H2	
E	P(Dolomite-IHC6-D3/D4)-C2-S2	
F	P(Dolomite-IHC7-D4)-C2-S2	
G	P(Dolomite-IHC8-D4)-C2-S2	
H	Not investigated (Agricultural)	

CERTIFIED BY: _____ (SIGNATURE)	⊕ PERCUSSION BOREHOLE
_____ (PR ENG NO)	○ TEST PIT
_____ (DATE)	

CITY OF TSHWANE METROPOLITAN MUNICIPALITY			
PLAN NUMBER: DRAFT 3		APPLICANT: _____	
NO	DATE	AMENDMENTS	
REV 0	JULY 2024	SUBMISSION	

CONTOURS:

THE CONTOURS ON THIS LAYOUT IS IN ACCORDANCE WITH THE REQUIREMENTS OF REGULATION 18(1) OF THE TOWN-PLANNING AND TOWNSHIPS ORDINANCE, 1986 (ORDINANCE 15 OF 1986). THIS CONTOUR SURVEY WAS COMPLIED BY:

CONTOUR INTERVAL: ?? METER

CERTIFIED BY: _____ (SIGNATURE)

_____ (PR ENG NO)

_____ (DATE)

FLOOD LINE CERTIFICATE:

THIS IS TO CERTIFY THAT IN ACCORDANCE WITH CLAUSE 144 OF THE NATIONAL WATER ACT (ACT 36 OF 1998), THAT: THE TOWNSHIP IS AFFECTED BY THE 1 IN EVERY 50 OR 1 IN EVERY 100 YEAR FLOOD LINE.

CERTIFIED BY: _____ (SIGNATURE)

_____ (PR ENG NO)

_____ (DATE)